Evenement	Evenementdatum	Versie-datum	Noordpijl
Op de Brink voor Betondorp	**1-4 -2024**	**2023 0424**	
Organisator	Locatie	Set	Formaat / Schaal
Stichting Dorpsfeest	**Brink Betondorp**	Set20230424 Github.com/situatietekening	**A2** / **1: 500**

10x10m2

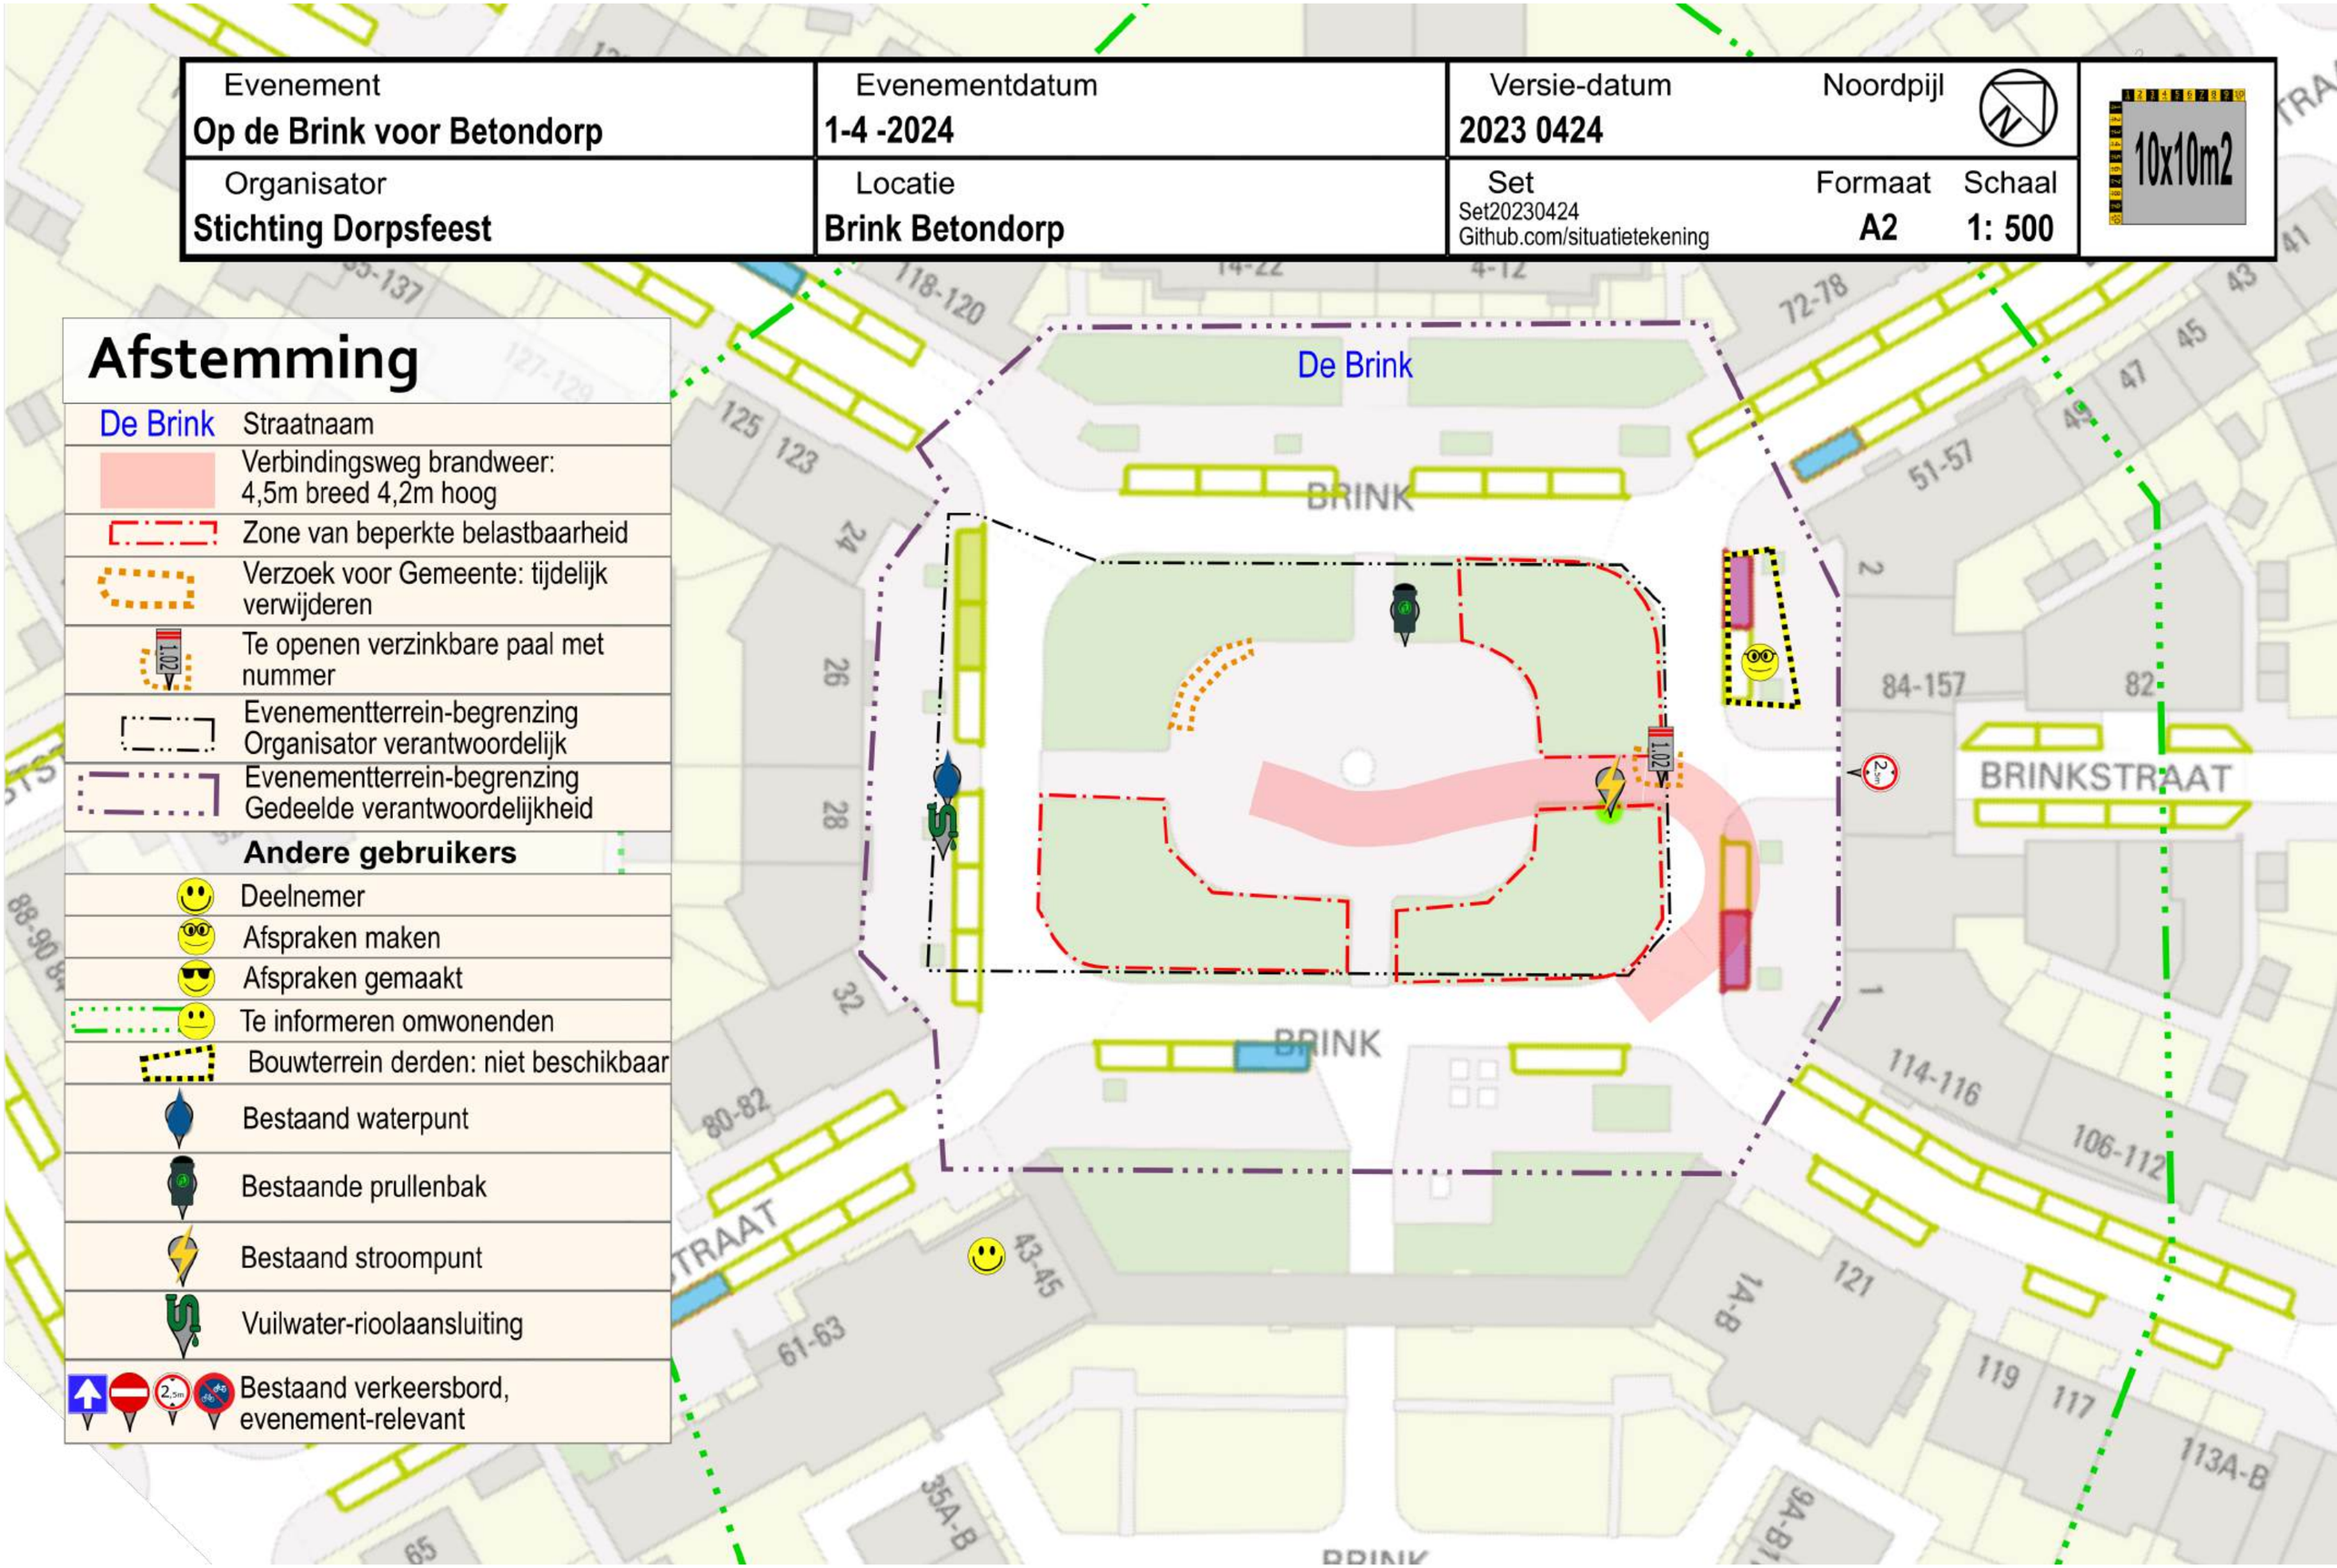

Afstemming

De Brink	Straatnaam
	Verbindingsweg brandweer: 4,5m breed 4,2m hoog
	Zone van beperkte belastbaarheid
	Verzoek voor Gemeente: tijdelijk verwijderen
1.02	Te openen verzinkbare paal met nummer
	Evenementterrein-begrenzing Organisator verantwoordelijk
	Evenementterrein-begrenzing Gedeelde verantwoordelijkheid
	Andere gebruikers
	Deelnemer
	Afspraken maken
	Afspraken gemaakt
	Te informeren omwonenden
	Bouwterrein derden: niet beschikbaar
	Bestaand waterpunt
	Bestaande prullenbak
	Bestaand stroompunt
	Vuilwater-rioolaansluiting
2,5m	Bestaand verkeersbord, evenement-relevant

Evenement	Evenementdatum	Versie-datum	Noordpijl
Op de Brink voor Betondorp	**1-4 -2024**	**2023 0424**	
Organisator	Locatie	Set	Formaat / Schaal
Stichting Dorpsfeest	**Brink Betondorp**	Set20230424 Github.com/situatietekening	**A2** / **1: 500**

10x10m2

Publieksplattegrond

Podium 6x5 m2	Podium met overkapping
	Bier-banken: 1,5x2,5 m2
	Foodtruck 4x6 m2
	Standaard marktkraam, dak: 4,4 x 2,5 m2
	Luchtkussen met toezichthouder 4x4 m2
RAS	Zweefmolen, diam 4m, vrije ruimte 2m RAS-Registratie
Gebakkraam	Hollandse Gebakkraam, uitgeklapt 7x4,5 m2
Schminken	Zone met kleine objecten tbv publieksfunctie
	Live muziek
WC /	Mobiel toilet / plaskruis,1 m2
WC	Toilet wagen 8x 2,5 m
	Schenkpunt met o.a. alcohol
	Eten niet-warm bereid
	Bakpunt met 2 m vrije ruimte (BGBOP 5.14)
	Glazen-inzamelbox
	Rest-afvalbak
	EHBO-punt: koffer + signing, BHV-ers
	Nooduitgangbord

Evenement	Evenementdatum	Versie-datum	Noordpijl
Op de Brink voor Betondorp	**1-4 -2024**	**2023 0424**	
Organisator	Locatie	Set	Formaat / Schaal
Stichting Dorpsfeest	**Brink Betondorp**	Set20230424 Github.com/situatietekening	**A2** / **1: 500**

10x10m2

Voorzieningen

- Easy-Up party-tent 3x3m2
- Pagode-tent 5x5 m2
- Aluhal (5x10 m2)
- Brandblusser aanwezig, 6kg
- Geluidsbox met geluidrichting
- Meetpunt geluid: 1 m van de gevel
- Kabels / leidingen met afdekking
- Rijplaten: kunsstof 6x1,5 m2 'blijft liggen' / 'opbouw-route'
- Vaste positie beveiliger
- Vaste positie toezichthouder
- Front of House / geluidtechniek
- Centrale Post
- Noodverlichting en -signing
- Netto vloer-oppervlakte (300 m2) / Maximaal aantal personen (200 p)
- Gekoppelde stoelenrij, (BGBOP 5.17) stoel 50 cm + vrije ruimte 45 cm
- Bankentribune, lbh 6 x 4,2 x 1,2 m
- Gangpad vrije doorgang 1,1 m (BGBOP 5.18)
- Dranghek: 2,50m lang, 1m hoog
- Bouwhek 3,5 meter lang, gezeild: groen / wit / zwart / niet
- Bouwhek-poort met wiel 3,5 m breed
- Constructienaam — Naam van constructie / bouwsel, Constructie-gegevens COBc Richtlijn

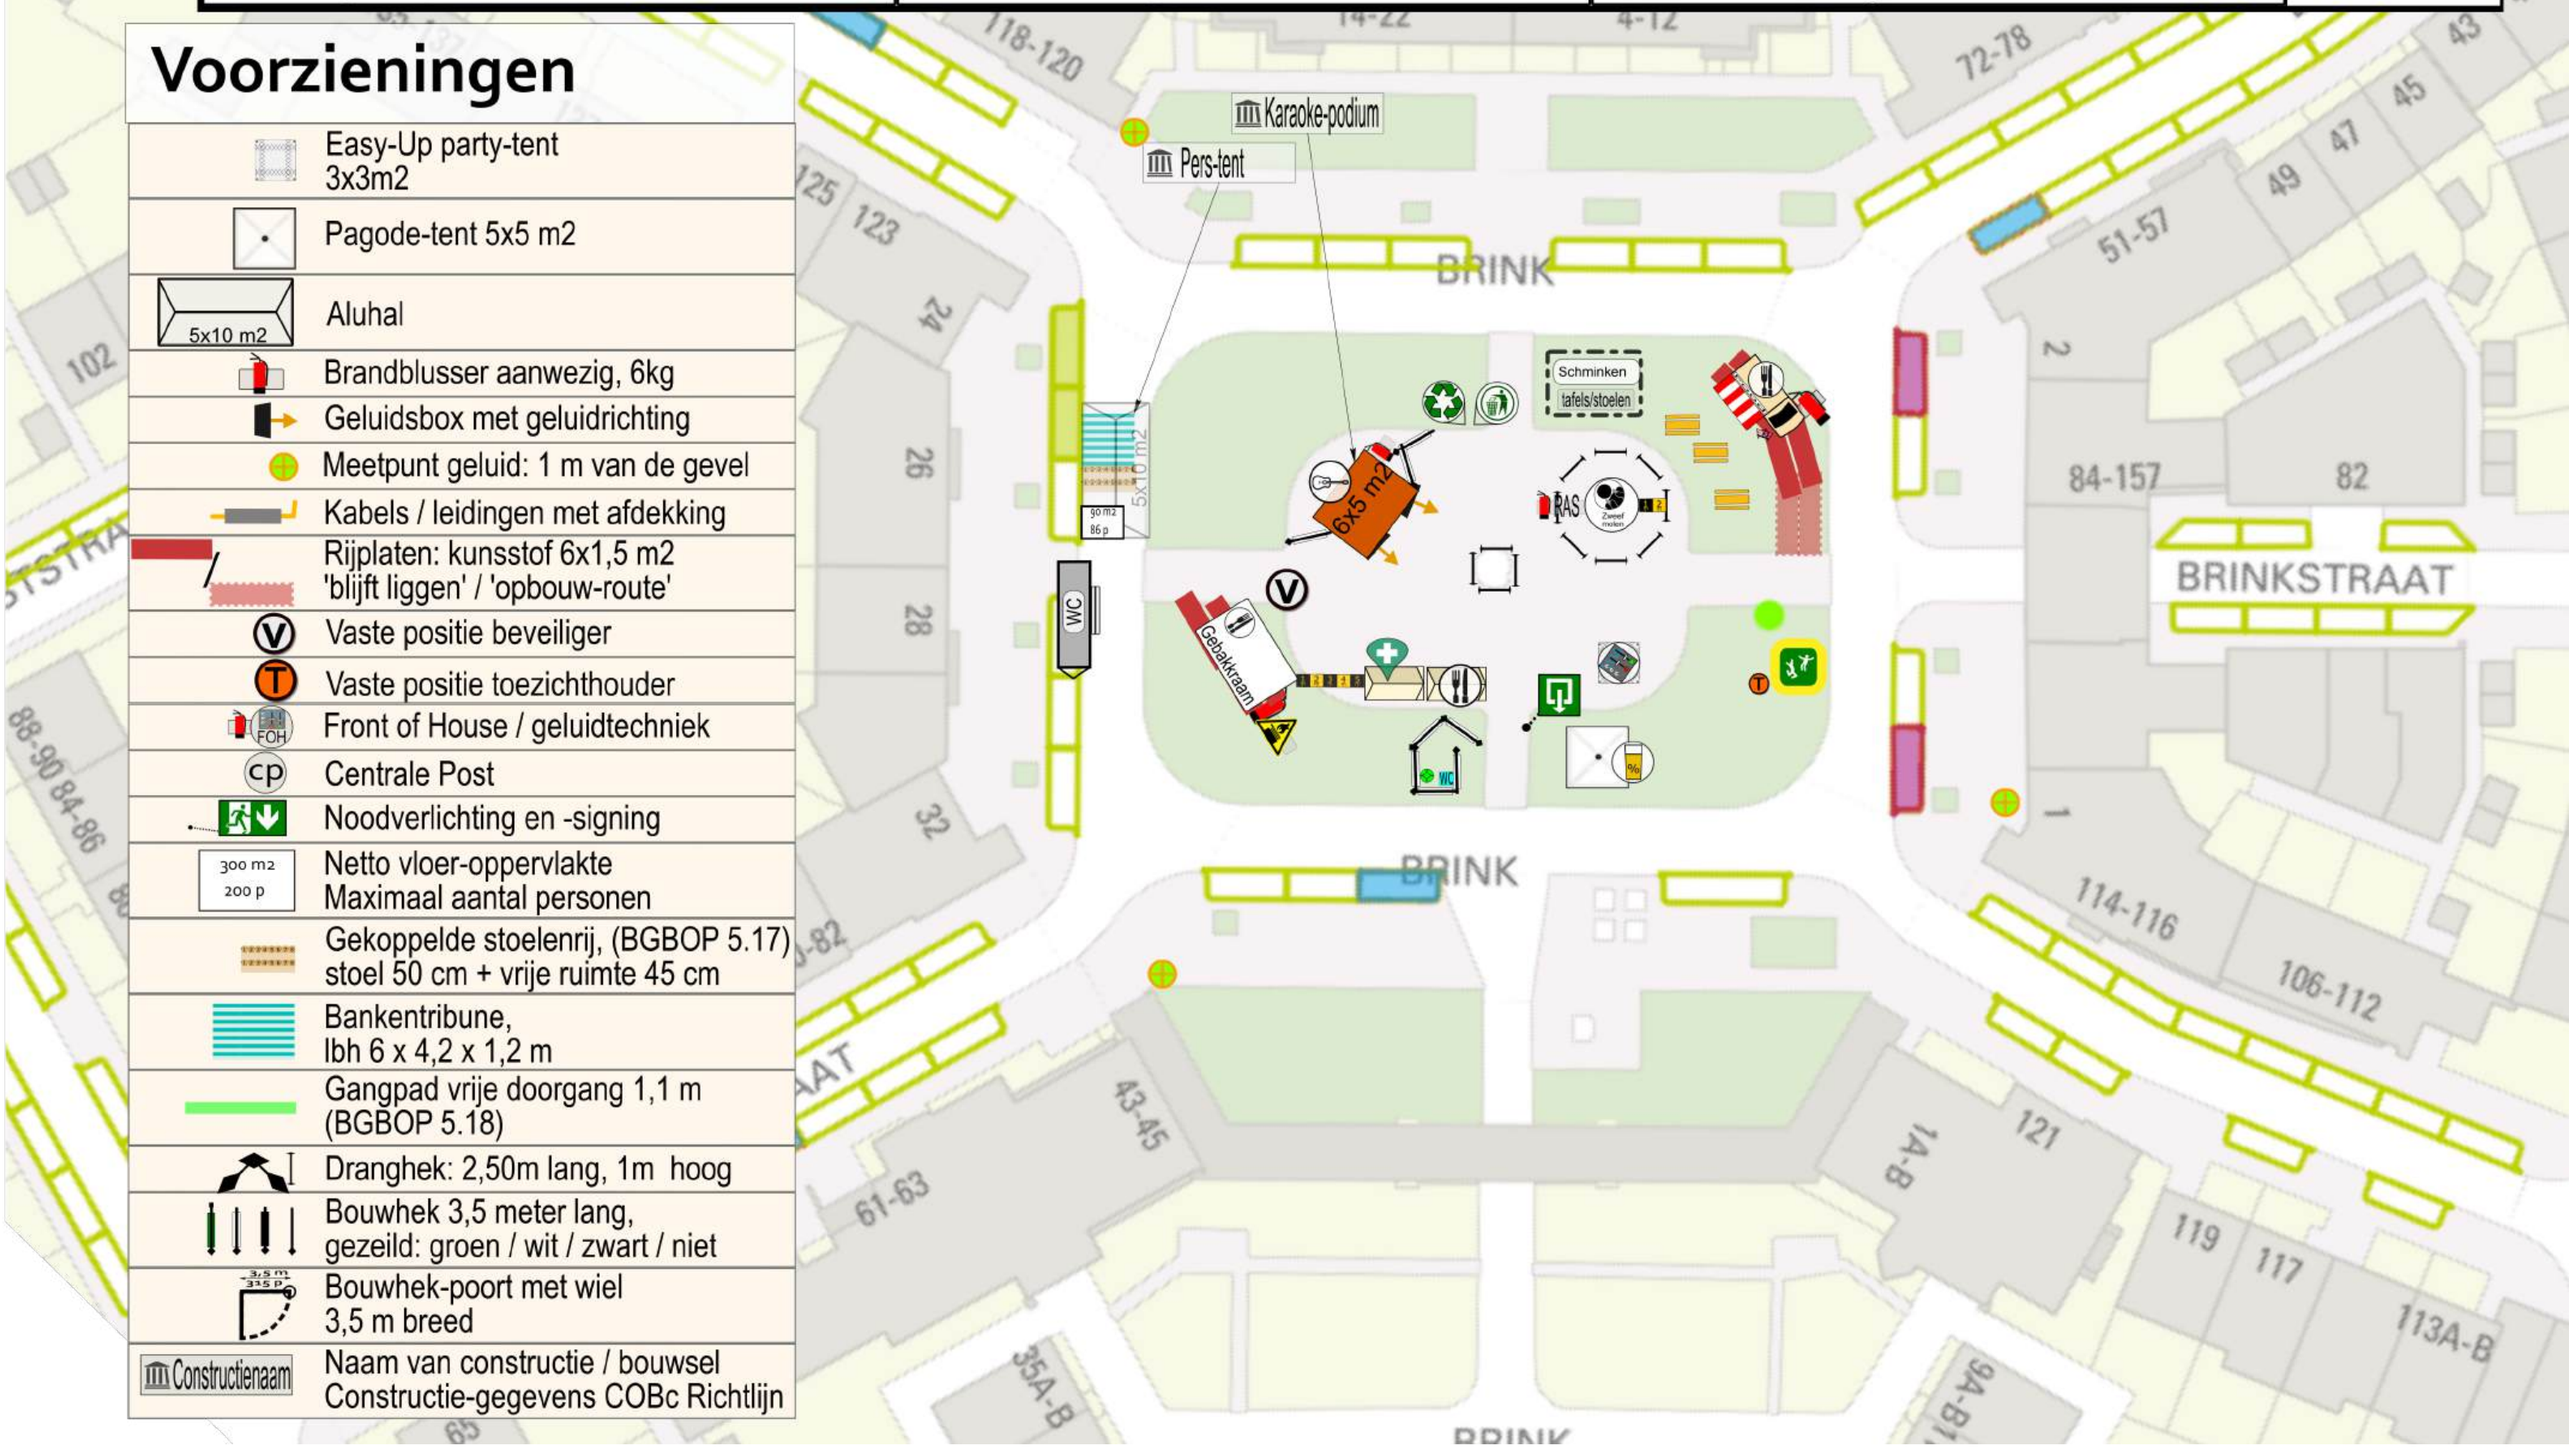

Evenement	Evenementdatum	Versie-datum	Noordpijl
Op de Brink voor Betondorp	**1-4 -2024**	**2023 0424**	
Organisator	Locatie	Set	Formaat / Schaal
Stichting Dorpsfeest	**Brink Betondorp**	Set20230424 Github.com/situatietekening	**A2** / **1: 500**

10x10m2

Verkeersplan

	Bezoekersroute
	Vluchtroute
	Aanrijroute hulpdiensten
	1 te reserveren parkeerplaats
	5 te reserveren parkeerplaatsen
	Omleiding reguliere gebruikers
1a	Verkeerspost-nummer
	Verkeershekken met C1 bord
S	Steward voor deelnemers/bezoekers
H	Hekbewaker
	Evenementen verkeersregelaar
	Beroeps verkeersregelaar
K+R	Te plaatsen Kiss+Ride bord
TAXI	Te plaatsen bord Taxi
i.v.m. evenement 3 febr afgesloten Brink nr 28 - 32	Te plaatsen omleidingsbord
i.v.m. evenement 3 febr afgesloten Brink nr 28 - 32	Te plaatsen omleidingsbord fietsers voetgangers

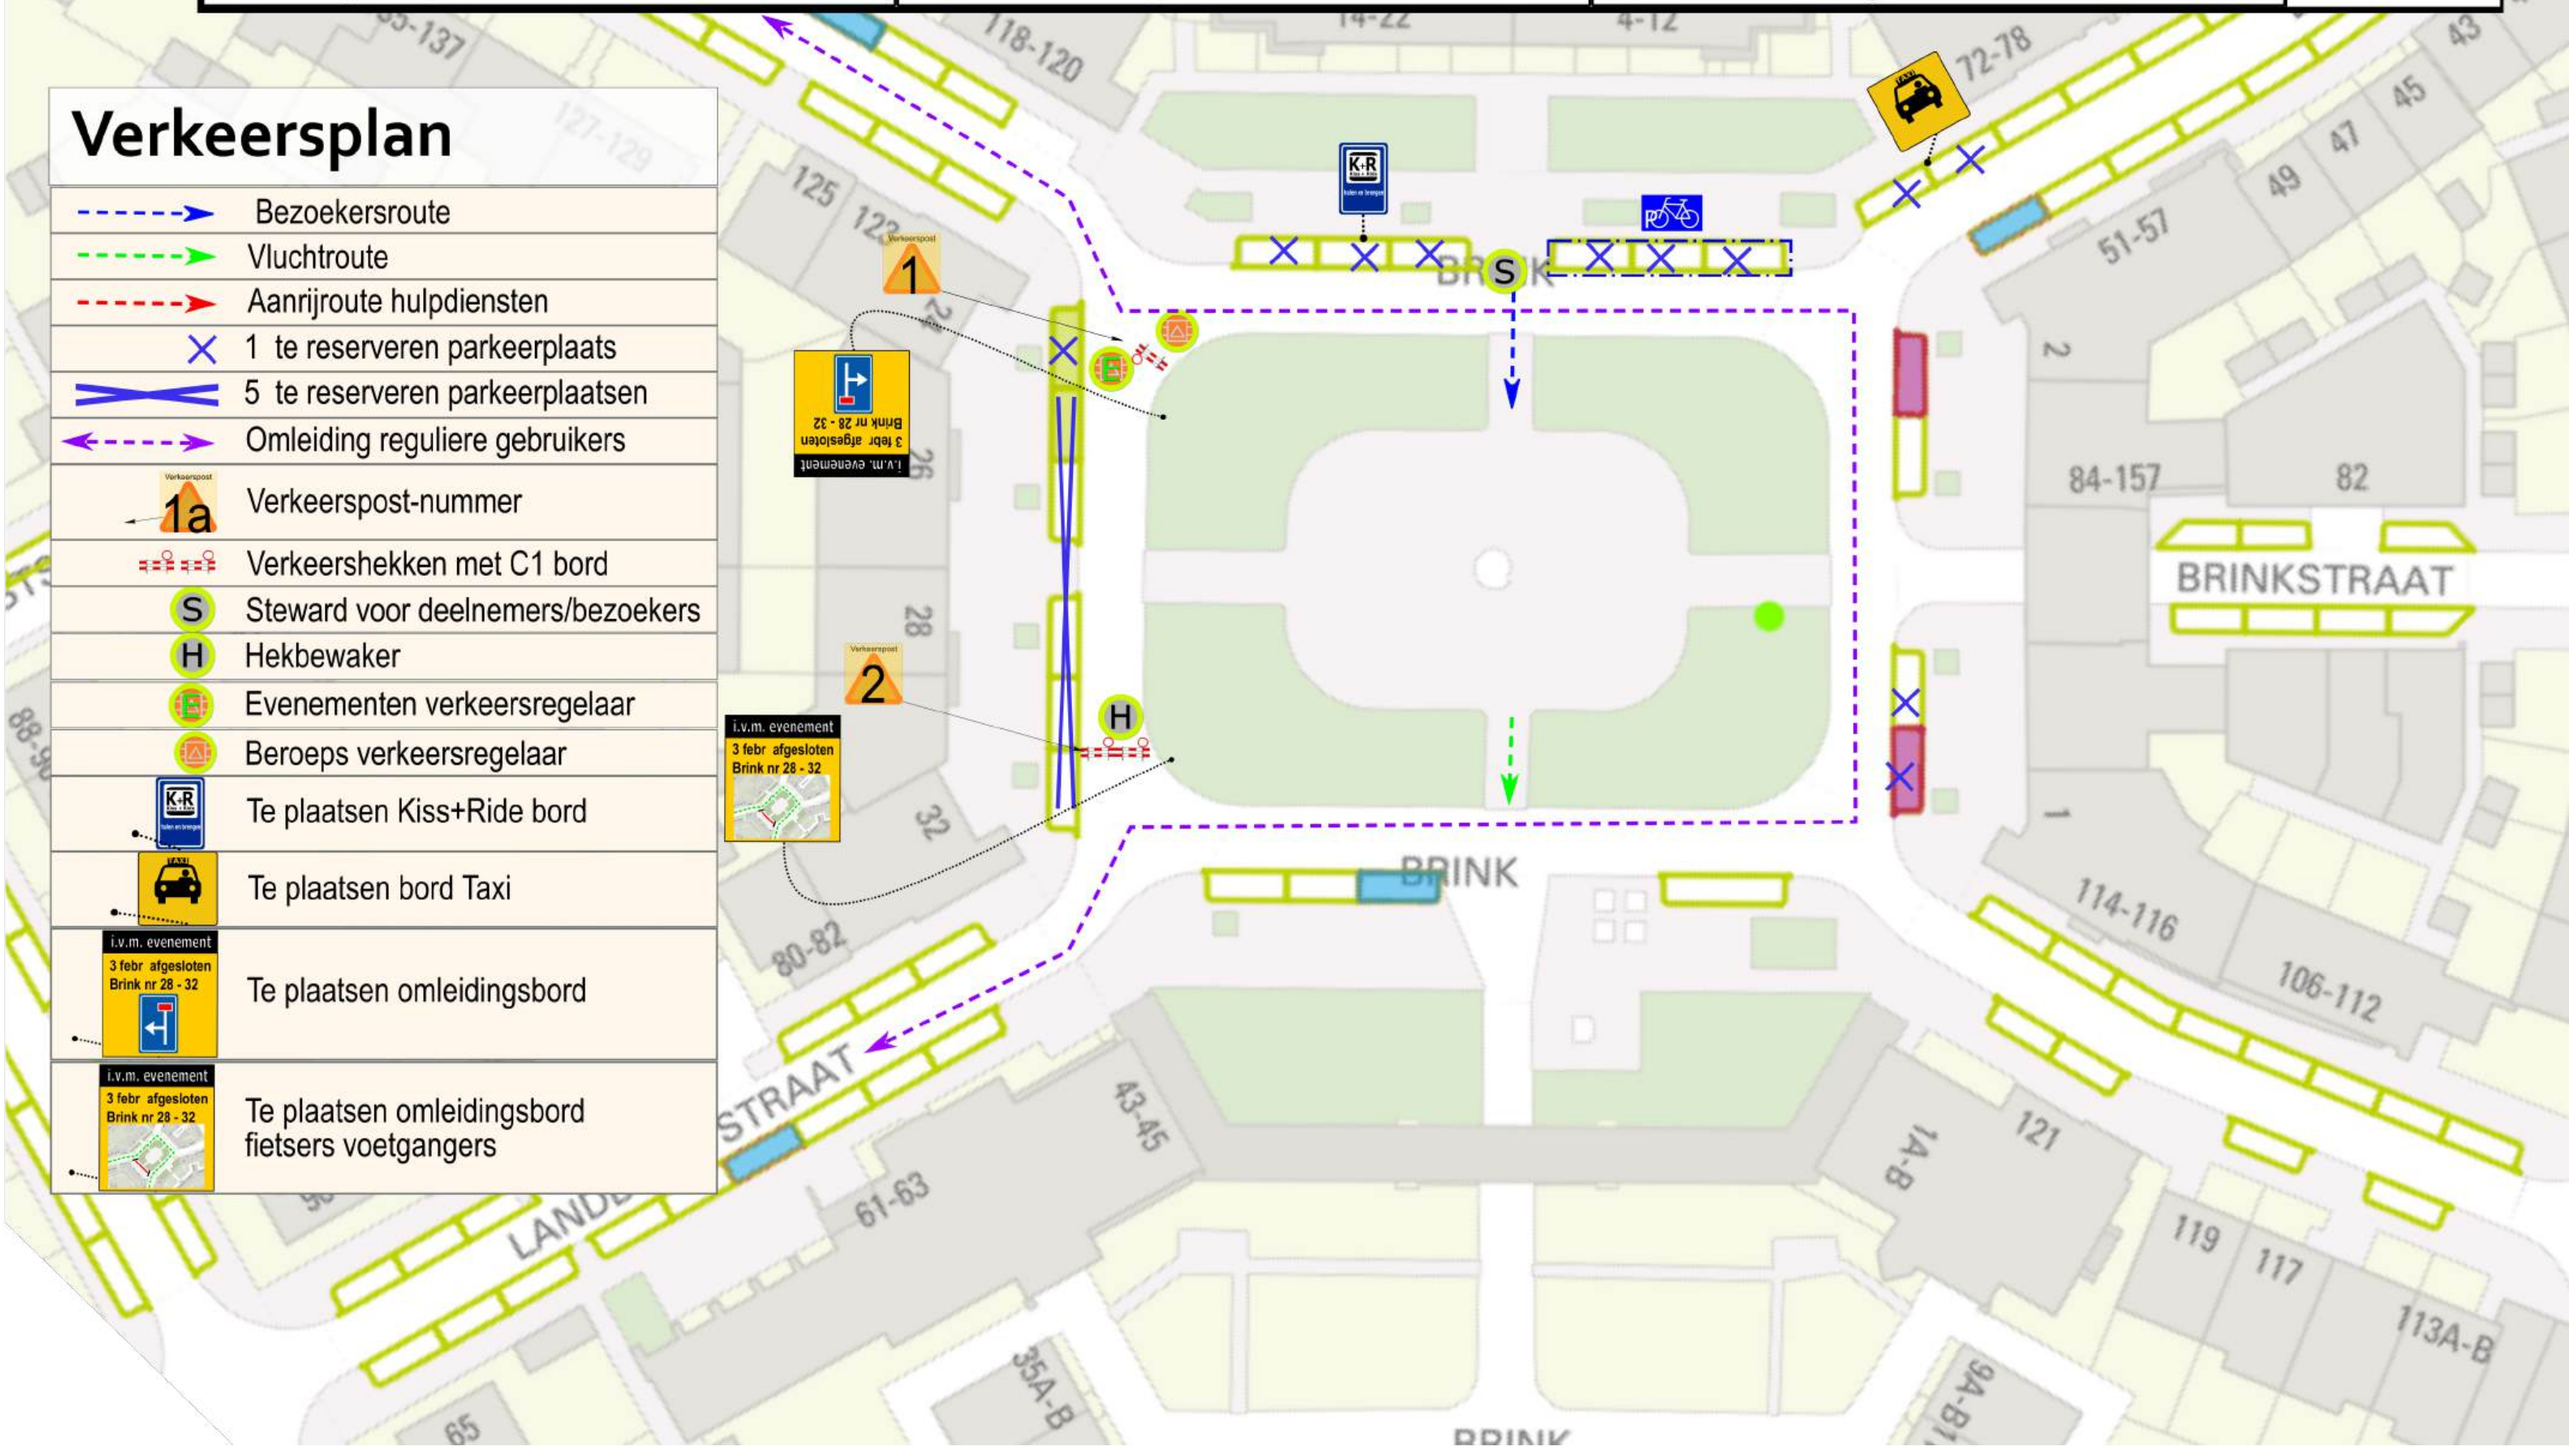

Evenement	Evenementdatum	Versie-datum	Noordpijl
Op de brink voor Betondorp	**1-4-2023**	**2023 0424**	N
Organisator	Locatie	Set	Formaat / Schaal
Stichting Betondorpsfeest	**Brink Betondorp**	Set20230424 Github.com/situatietekening	**A2** / **1: 500**

10x10m2

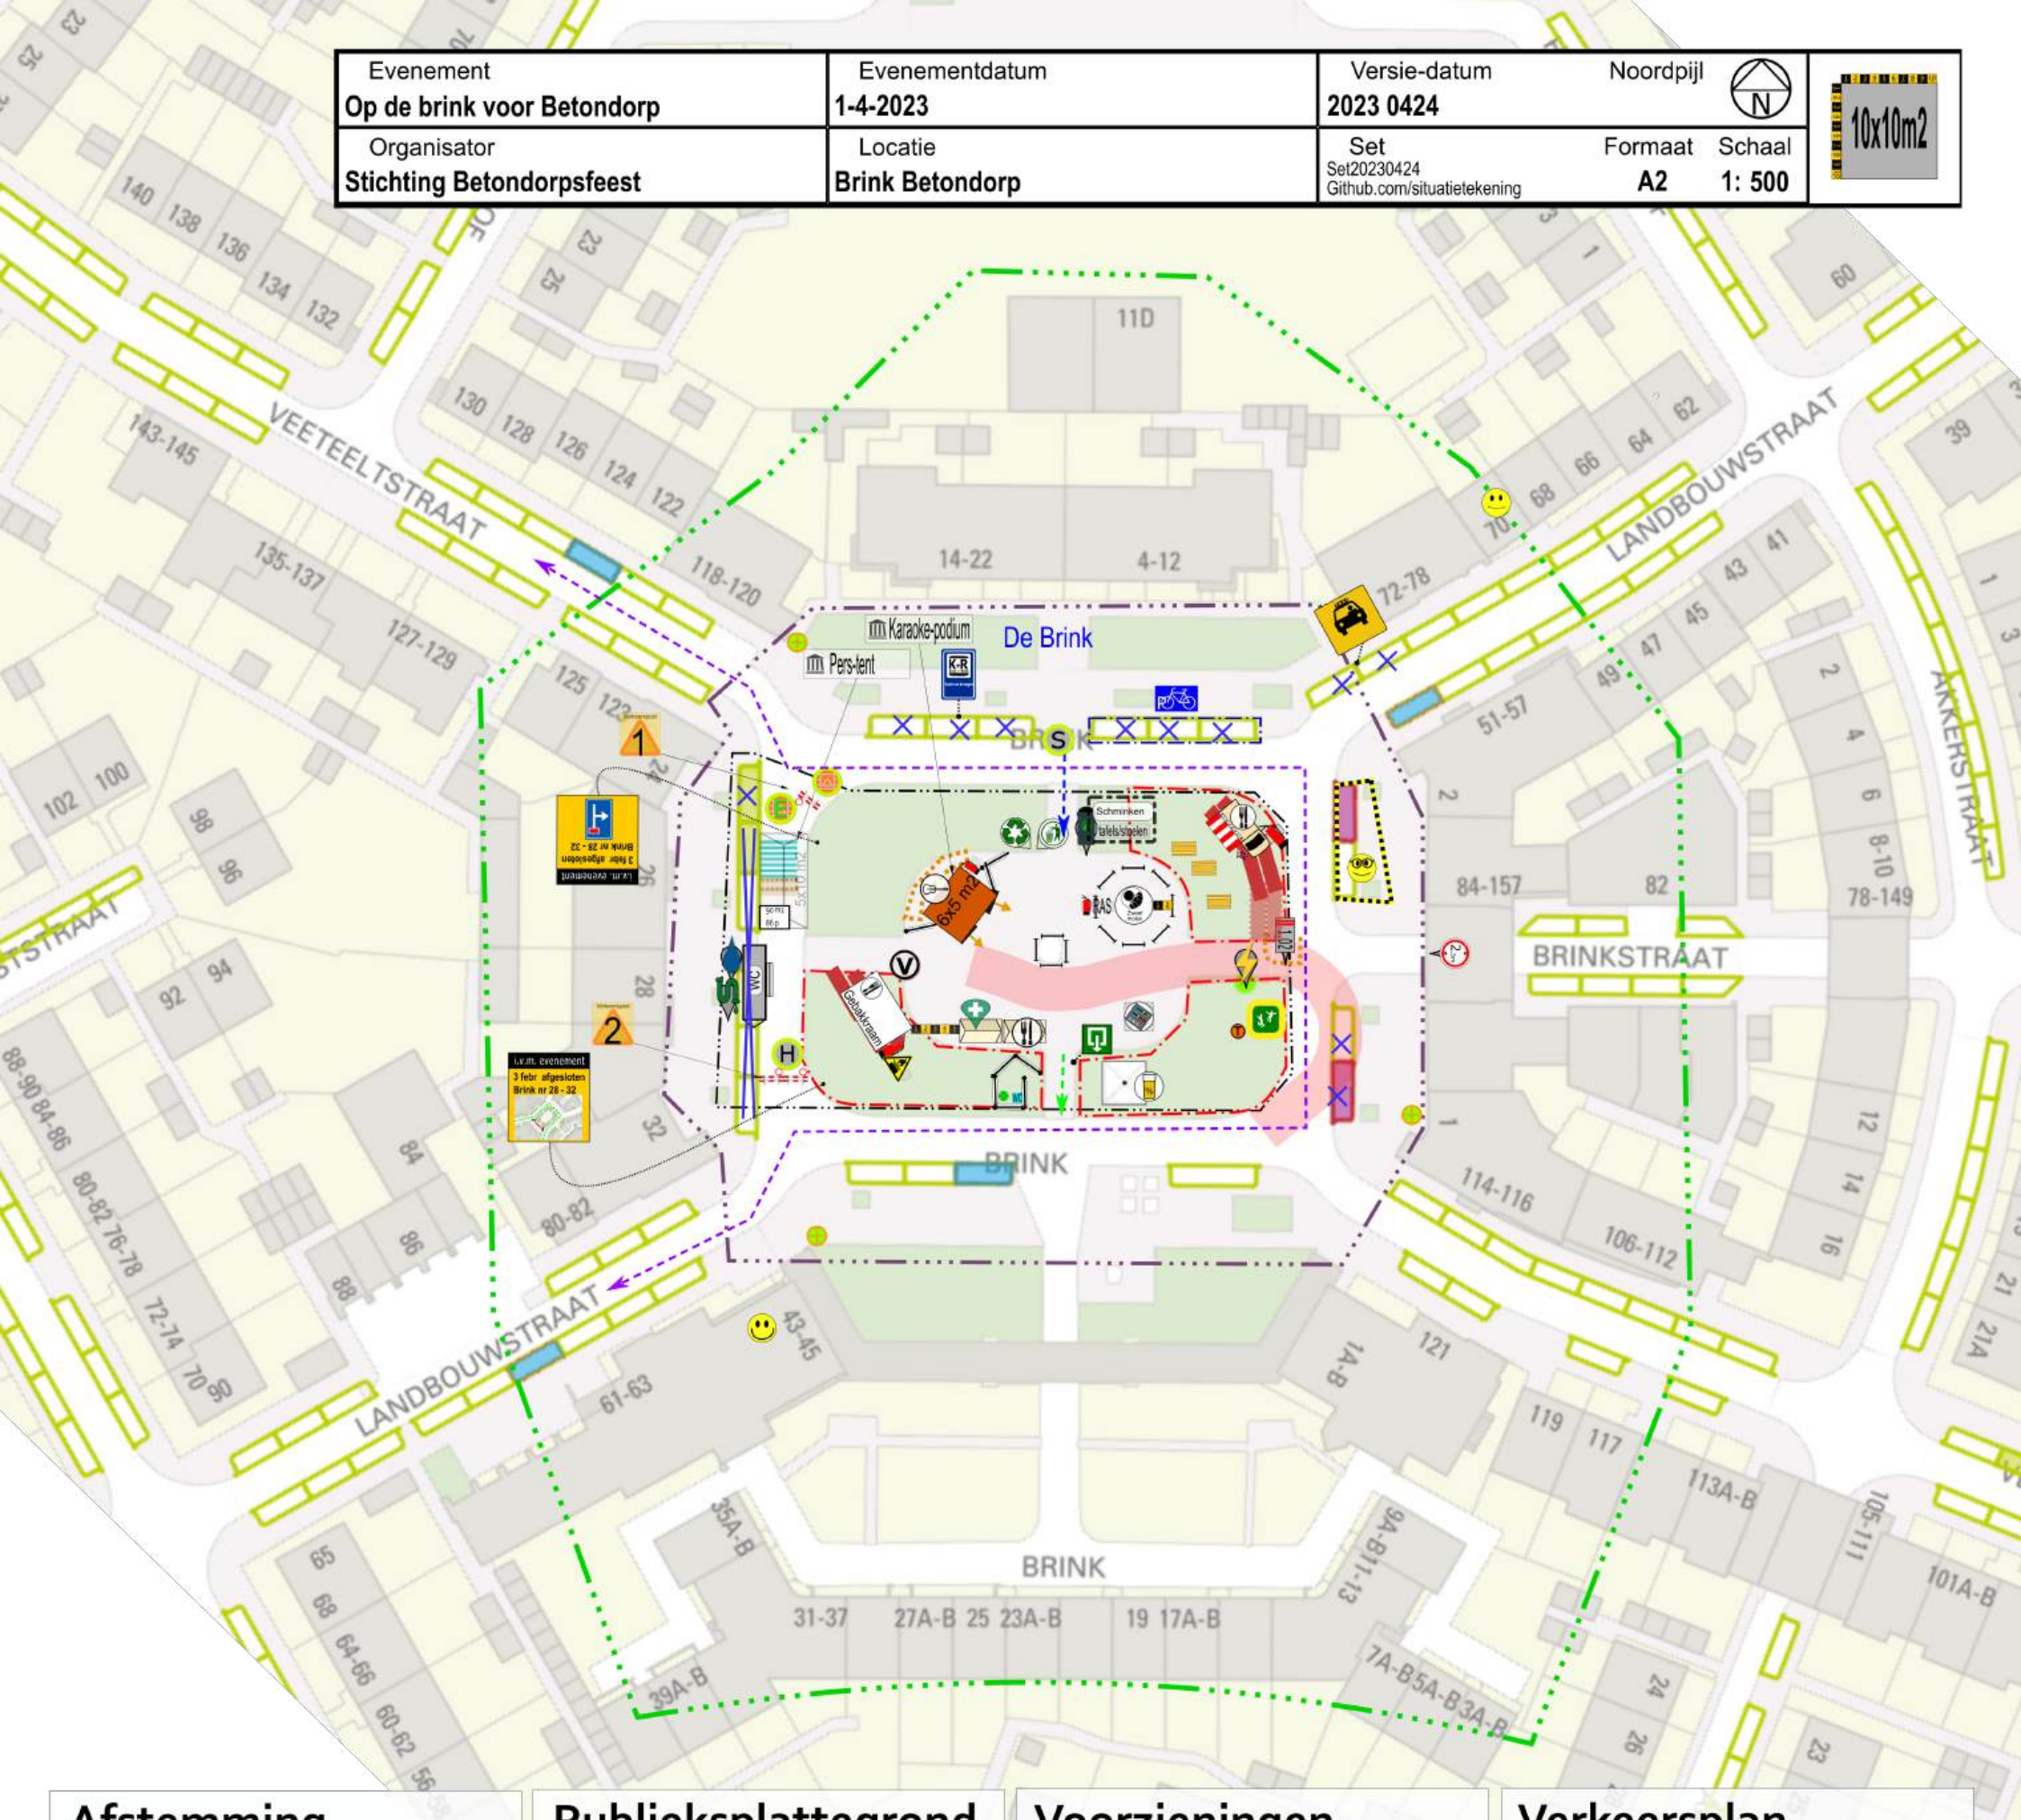

Afstemming

De Brink	Straatnaam
	Verbindingsweg brandweer: 4,5m breed 4,2m hoog
	Zone van beperkte belastbaarheid
	Verzoek voor Gemeente: tijdelijk verwijderen
	Te openen verzinkbare paal met nummer
	Evenementterrein-begrenzing Organisator verantwoordelijk
	Evenementterrein-begrenzing Gedeelde verantwoordelijkheid
Andere gebruikers	
	Deelnemer
	Afspraken maken
	Afspraken gemaakt
	Te informeren omwonenden
	Bouwterrein derden: niet beschikbaar
	Bestaand waterpunt
	Bestaande prullenbak
	Bestaand stroompunt
	Vuilwater-rioolaansluiting
	Bestaand verkeersbord, evenement-relevant

Publieksplattegrond

Podium 6x5 m2	Podium met overkapping
	Bier-banken: 1,5x2,5 m2
	Foodtruck 4x6 m2
	Standaard marktkraam, dak: 4,4 x 2,5 m2
	Luchtkussen met toezichthouder 4x4 m2
RAS	Zweefmolen, diam 4m, vrije ruimte 2m RAS-Registratie
Gebakkraam	Hollandse Gebakkraam, uitgeklapt 7x4,5 m2
Schminken	Zone met kleine objecten tbv publieksfunctie
	Live muziek
	Mobiel toilet / plaskruis,1 m2
WC	Toilet wagen 8x 2,5 m
	Schenkpunt met o.a. alcohol
	Eten niet-warm bereid
	Bakpunt met 2 m vrije ruimte (BGBOP 5.14)
	Glazen-inzamelbox
	Rest-afvalbak
	EHBO-punt: koffer + signing, BHV-ers
	Nooduitgangbord

Voorzieningen

	Easy-Up party-tent 3x3m2
	Pagode-tent 5x5 m2
5x10 m2	Aluhal
	Brandblusser aanwezig, 6kg
	Geluidsbox met geluidrichting
	Meetpunt geluid: 1 m van de gevel
	Kabels / leidingen met afdekking
	Rijplaten: kunststof 6x1,5 m2 'blijft liggen' / 'opbouw-route'
V	Vaste positie beveiliger
T	Vaste positie toezichthouder
FOH	Front of House / geluidtechniek
cp	Centrale Post
	Noodverlichting en -signing
300 m2 200 p	Netto vloer-oppervlakte Maximaal aantal personen
	Gekoppelde stoelenrij, (BGBOP 5.17) stoel 50 cm + vrije ruimte 45 cm
	Bankentribune, lbh 6 x 4,2 x 1,2 m
	Gangpad vrije doorgang 1,1 m (BGBOP 5.18)
	Dranghek: 2,50m lang, 1m hoog
	Bouwhek 3,5 meter lang, gezeild: groen / wit / zwart / niet
3,5 m 245 p	Bouwhek-poort met wiel 3,5 m breed
Constructienaam	Naam van constructie / bouwsel Constructie-gegevens COBc Richtlijn

Verkeersplan

	Bezoekersroute
	Vluchtroute
	Aanrijroute hulpdiensten
	1 te reserveren parkeerplaats
	5 te reserveren parkeerplaatsen
	Omleiding reguliere gebruikers
1a	Verkeerspost-nummer
	Verkeershekken met C1 bord
S	Steward voor deelnemers/bezoekers
H	Hekbewaker
	Evenementen verkeersregelaar
	Beroeps verkeersregelaar
K+R	Te plaatsen Kiss+Ride bord
	Te plaatsen bord Taxi
i.v.m. evenement 3 febr afgesloten Brink nr 28 - 32	Te plaatsen omleidingsbord
i.v.m. evenement 3 febr afgesloten Brink nr 28 - 32	Te plaatsen omleidingsbord fietsers voetgangers